
[3] Project Architecture

Sheet hierarchy and signal flow. Click a block or its page number to open the sheet.

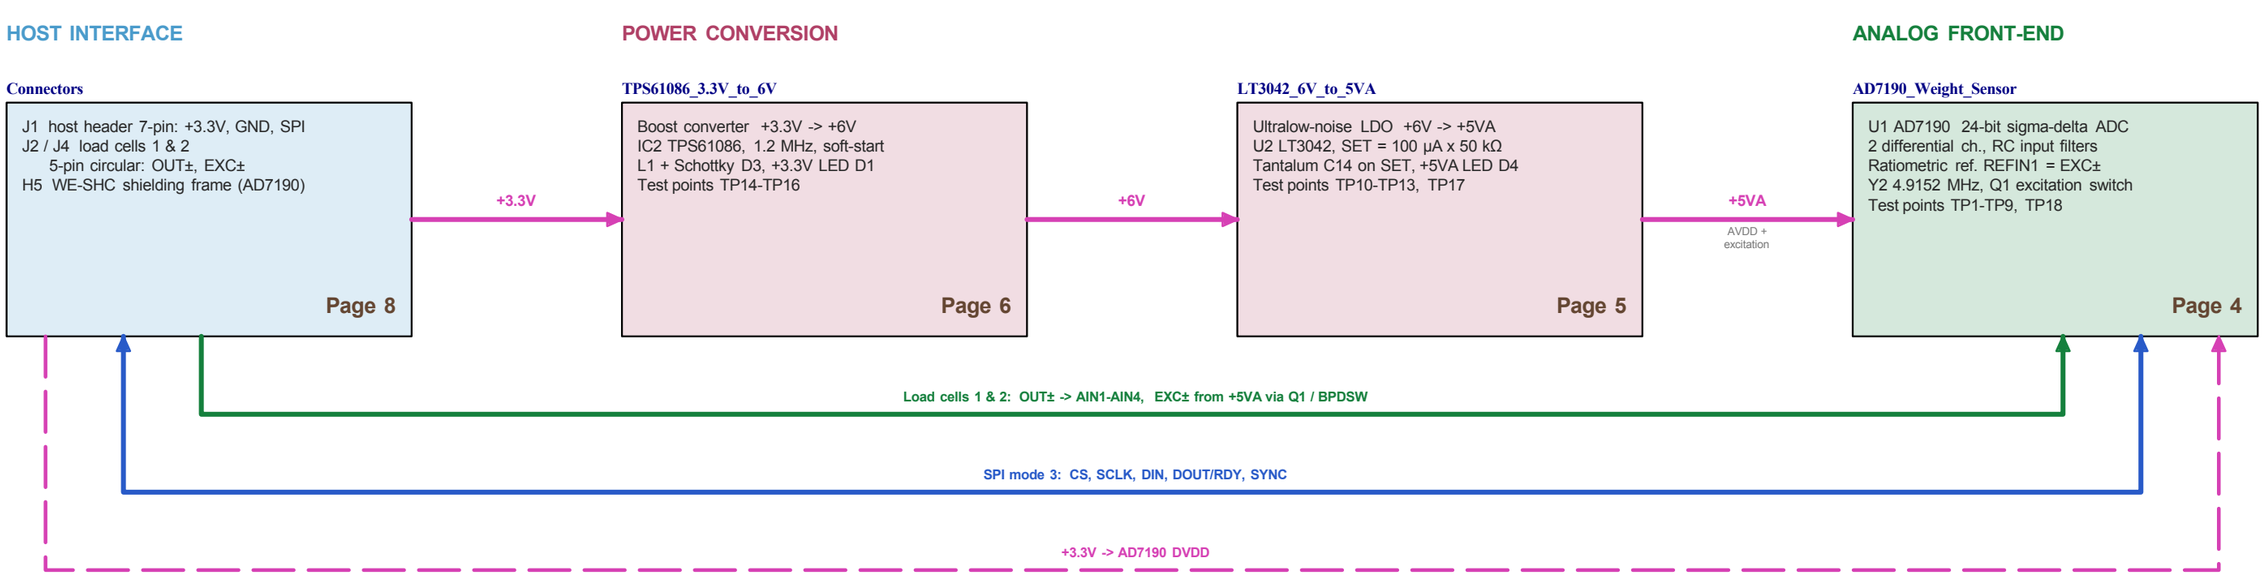

MECHANICAL

Holes, Fiducials

H1-H4 mounting holes
FID1-FID6 fiducials
No electrical function

Page 7

LEGEND

- Power rail
- Secondary supply
- Analog signal
- Digital / SPI

DOCUMENT INDEX

[1] Title Page
[2] Block Diagram
[3] Project Architecture
[4] AD7190 Weight Sensor
[5] LT3042 LDO 6V -> 5VA
[6] TPS61086 Boost 3V3 -> 6V
[7] Holes, Fiducials
[8] Connectors
[9] Power Sequencing
[10] Revision History

Comments:	Company: OPEN THRUST LAB		Variant:	Git Hash: 349b121
	Board Name: AD7190		Project Name: OPEN_WEIGHT	
Sheet Title: Project Architecture	File Name: Project Architecture.kicad_sch	Designer: SIEBERT DIMITRY	Date: 2026-09-29	Revision: + (Unreleased)
Sheet Path: /Project Architecture/		Reviewer:	Size: A3	Sheet: 3 of 10