



[3] Project Architecture

Sheet hierarchy and signal flow. Click a block or its page number to open the sheet.

HOST INTERFACE

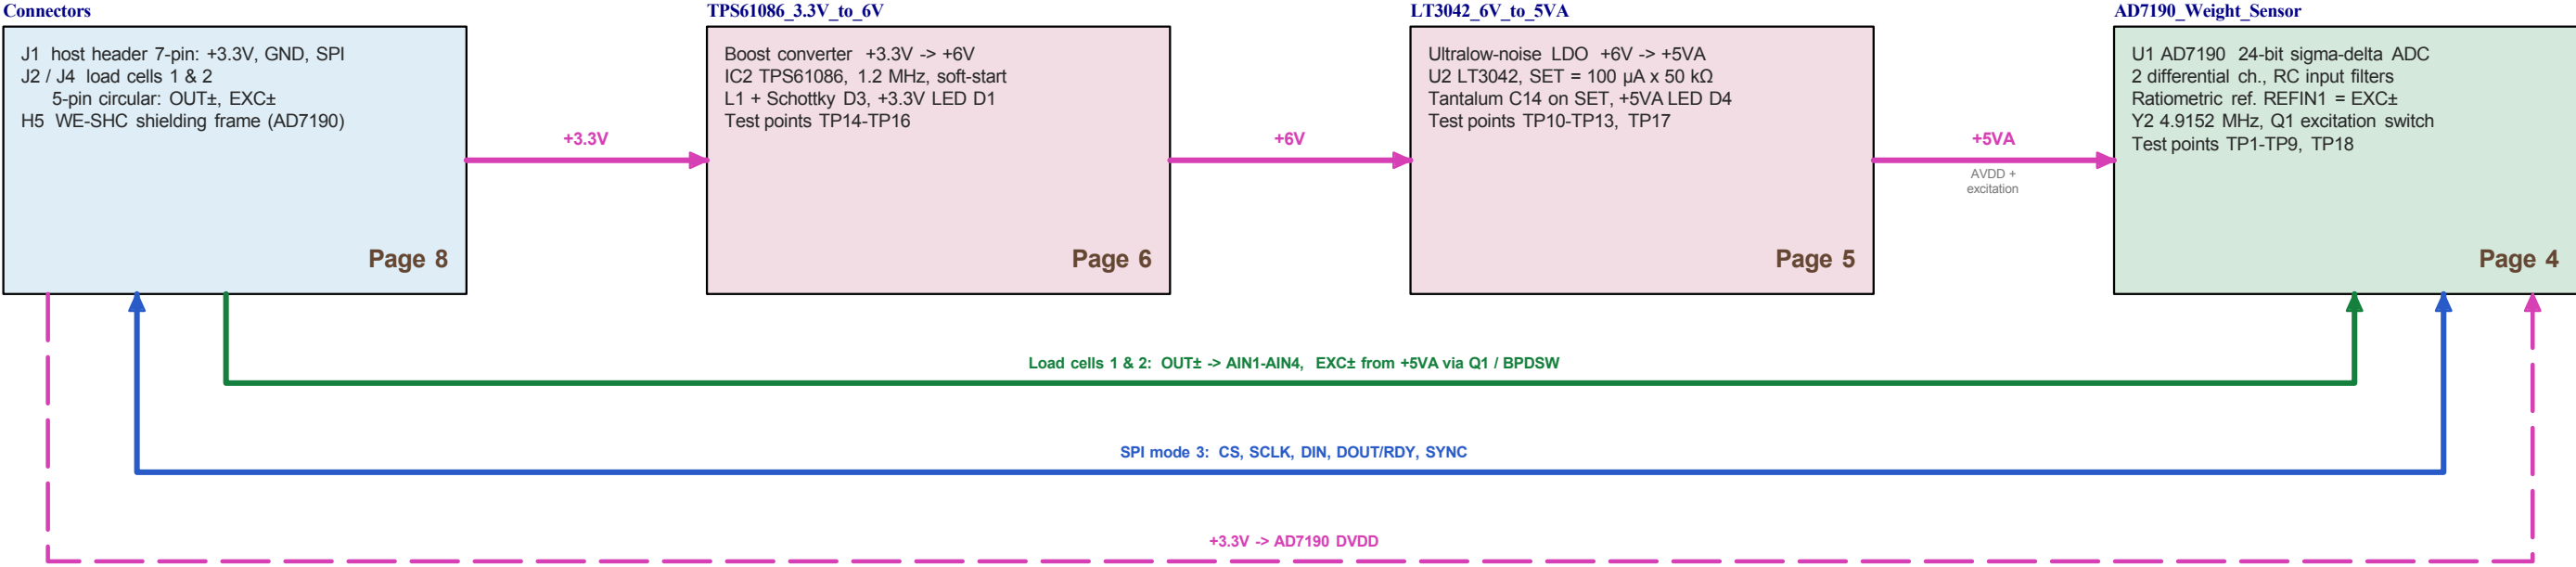

MECHANICAL

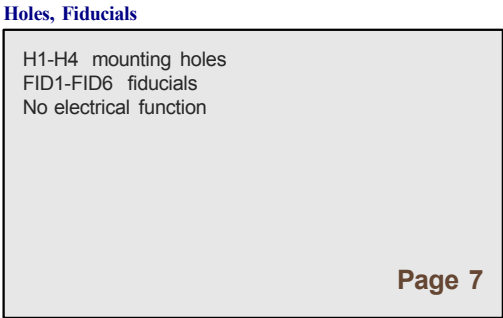

LEGEND

- Power rail
- Secondary supply
- Analog signal
- Digital / SPI

DOCUMENT INDEX

- [1] Title Page
- [2] Block Diagram
- [3] Project Architecture
- [4] AD7190 Weight Sensor
- [5] LT3042 LDO 6V -> 5VA
- [6] TPS61086 Boost 3V3 -> 6V
- [7] Holes, Fiducials
- [8] Connectors
- [9] Power Sequencing
- [10] Revision History



Comments:	Company: OPEN THRUST LAB		Variant:	Git Hash: b3867f9
	Board Name: AD7190		Project Name: OPEN_WEIGHT	
Sheet Title: Project Architecture	File Name: Project Architecture.kicad_sch	Designer: SIEBERT DIMITRY	Date: 2026-09-29	Revision: + (Unreleased)
Sheet Path: /Project Architecture/		Reviewer:	Size: A3	Sheet: 3 of 10